


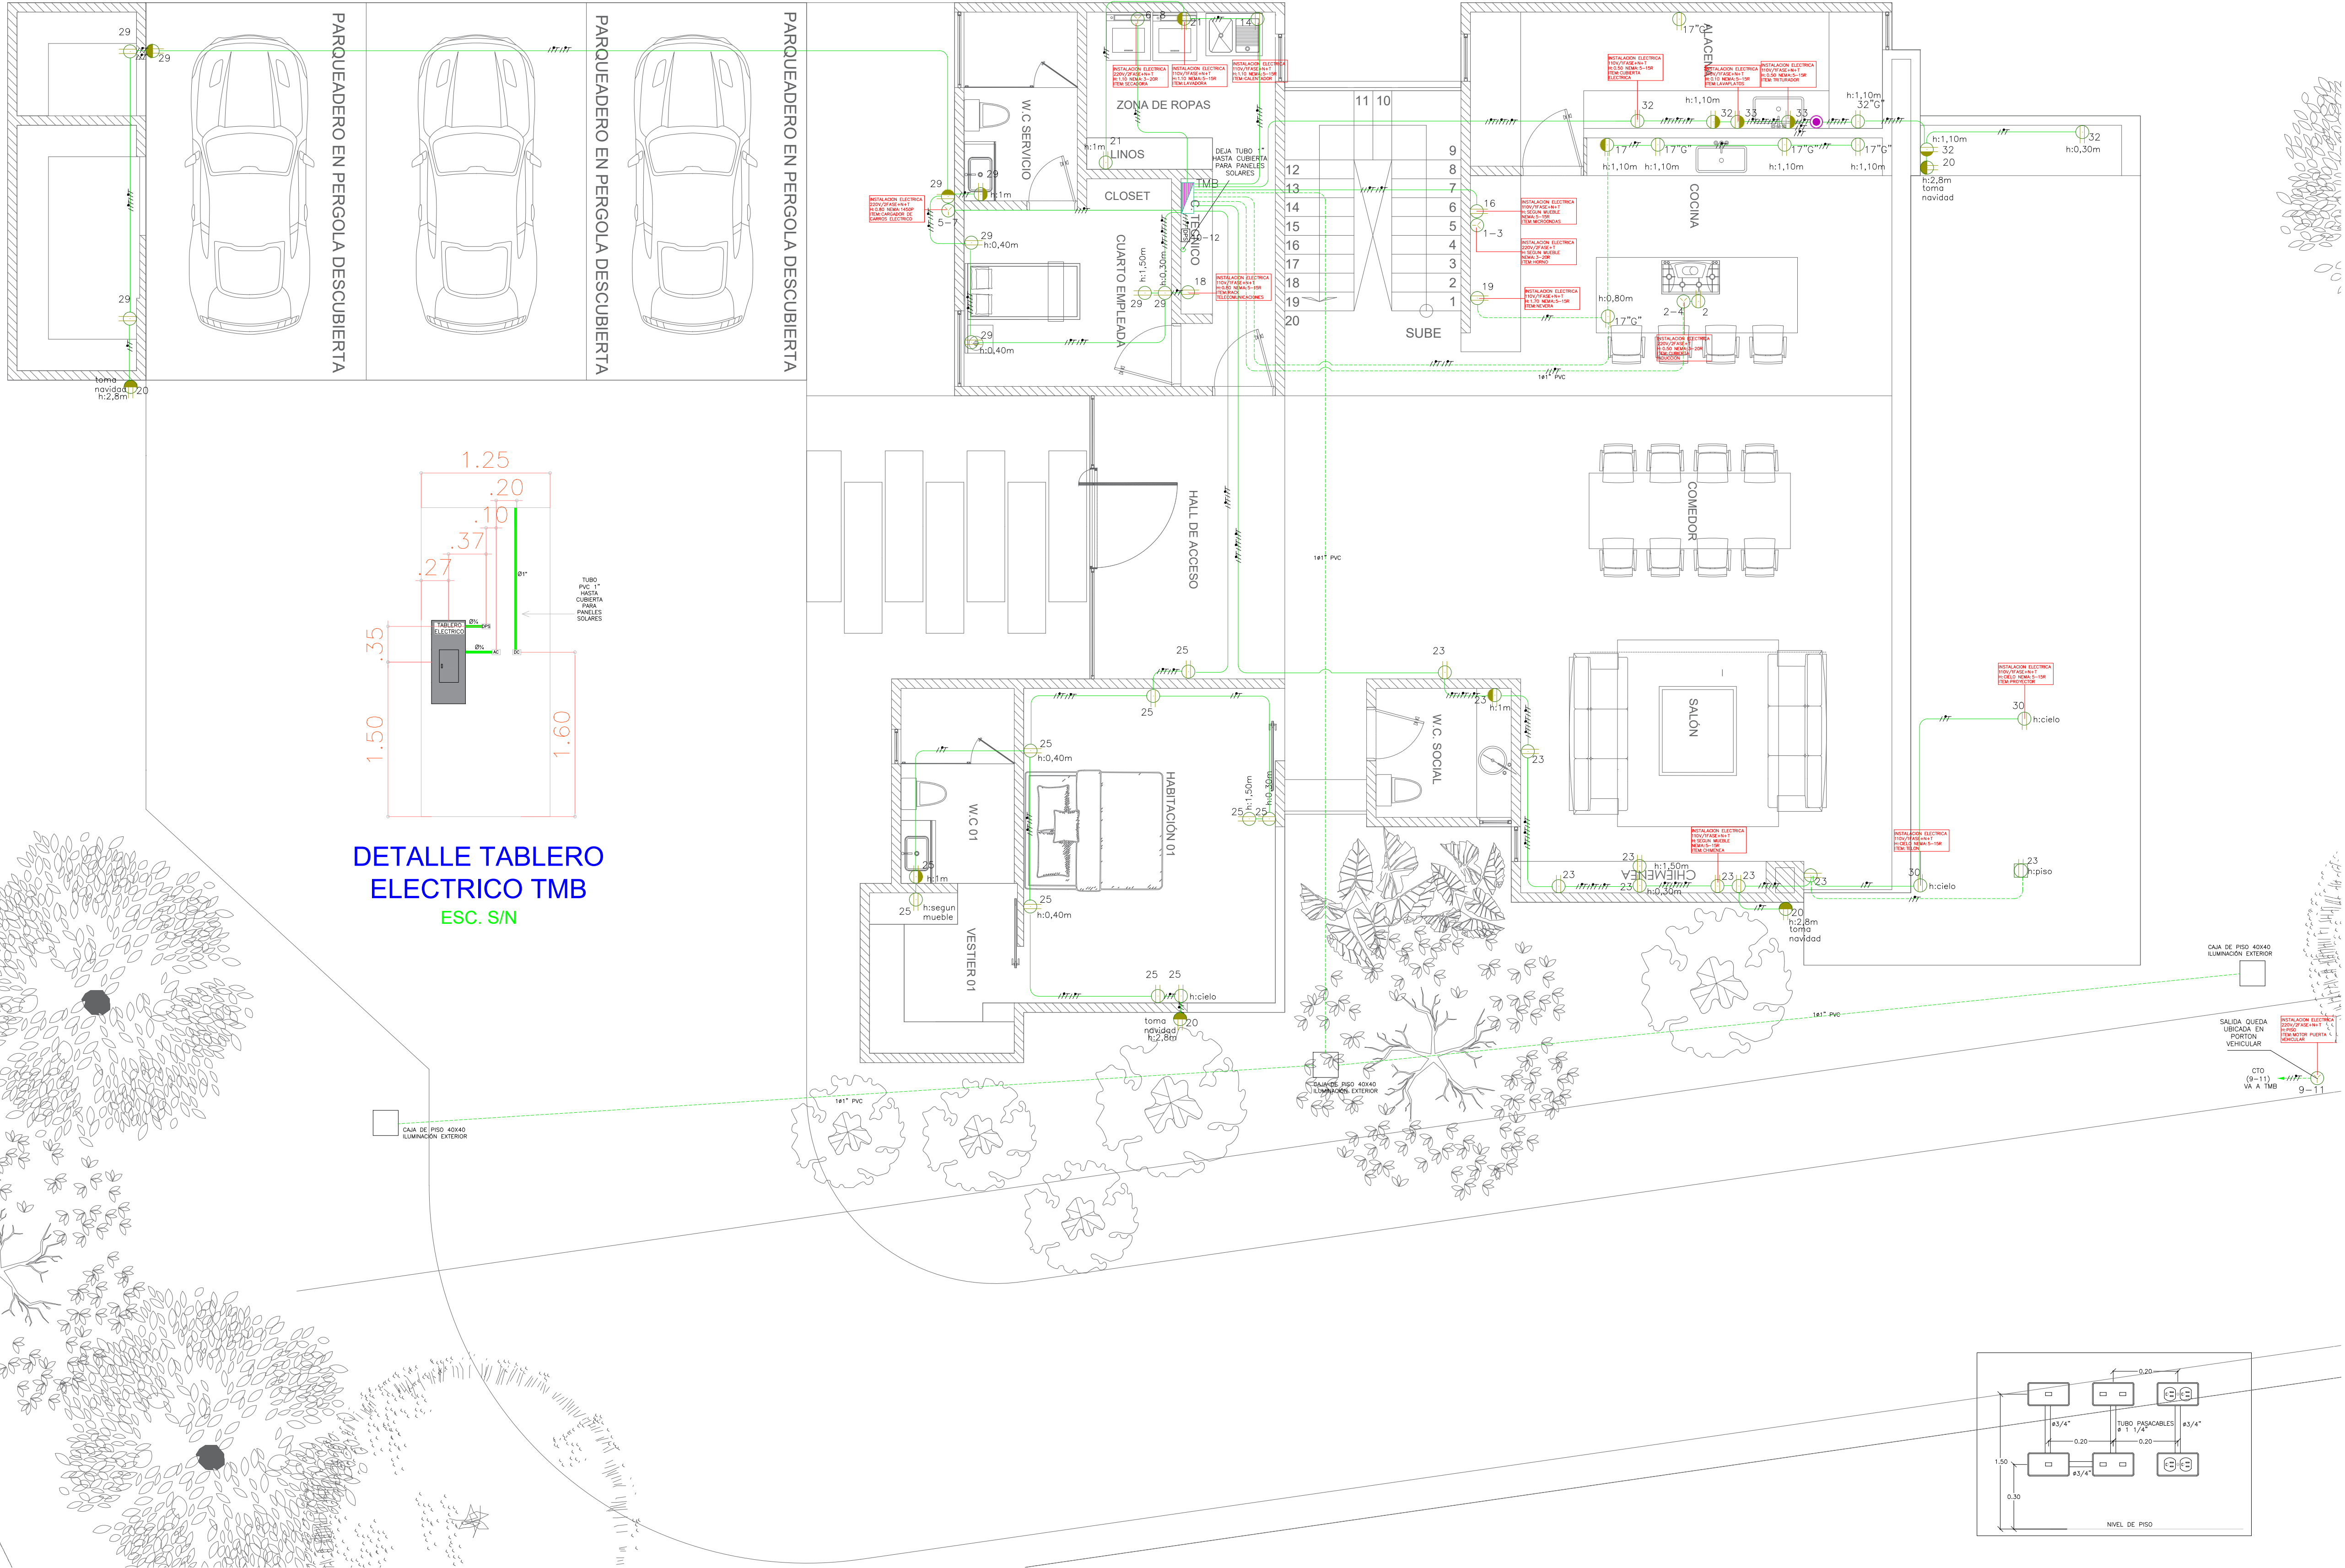

CONVENCIONES ELECTRICAS

|    |  |                                   |
|----|--|-----------------------------------|
| 1  |  | TOMA USO GENERAL                  |
| 2  |  | TOMA GFCI                         |
| 3  |  | TOMA 220V                         |
| 4  |  | TOMA TIPO INTEMPERIE              |
| 5  |  | TUBERIA CIELO O PARED             |
| 6  |  | TUBERIA POR PISO                  |
| 7  |  | CONDUCTORES FASE, NEUTRO Y TIERRA |
| 8  |  | TABLERO DE DISTRIBUCION           |
| 9  |  | CAMPANILLA                        |
| 10 |  | PULSADOR TIMBRE                   |
| 11 |  | TOMA DE PISO                      |

- NOTAS:
- TUBERIA Y ALAMBRE NO ESPECIFICADOS SON  $\phi 3/4"$  PVC No.12 AWG, THHN.
  - TUBERIA Y ALAMBRE NO ESPECIFICADOS EN CIELOS FALSOS PARA REDES SOBREPUESTAS SON  $\phi 3/4"$  INTERFLEX TIPO HFR  $\phi$  SCHEDULE 40 Y No.12 AWG, LSZH O LIBRE DE HALÓGENOS.
  - LAS CAJAS DONDE LLEGUE UN TUBO DE  $\phi 3/4"$   $\phi$  MAS SERÁN 4x4 INTERFLEX CON TAPA FLUSH.
  - LAS CAJAS PARA LAS SALIDAS DE, TELEVISION Y TELEFONO SERÁN 4x4 INTERFLEX CON TAPA FLUSH.
  - CODIGO DE COLORES: NEUTRO=BLANCO, TIERRA=VERDE. ESTOS COLORES NO PODRÁN SER UTILIZADOS PARA NINGUN OTRO CONDUCTOR.FASES: ROJO O NEGRO, DE ACUERDO A LO ESTIPULADO EN EL RETIE PARA TALEROS MONOFÁSICOS Y TRAFIO EN CONEXIÓN DELTA-ESTRELLA ATERRIZADO.
  - LA LINEA DE POLO A TIERRA IRA A LO LARGO DE TODA LA INSTALACION ELECTRICA EN CONDUCTOR COBRE, TW No.12 VERDE.
  - TODA SALIDA ELECTRICA DEBE QUEDAR A POR LO MENOS 30 cms DE LAS VALVULAS  $\phi$  SALIDAS DE GAS.
  - ALTURAS NO ESPECIFICADAS PARA SALIDAS SERA DE 30CM NIVEL PISO ACABADO.
  - LOS TUBOS POR CIELOS DEBERÁN SER EMT  $\phi$  SCH40 DE ACUERDO AL LITERAL 20.6.1.2 REQUISITOS DE INSTALACIÓN LITERAL H. NO SE DEBEN INSTALAR TUBERÍAS NO METÁLICAS LIVIANAS (TIPO A), EXPUESTAS NI EN CIELOS FALSOS; SOLO SE ADMITEN SI VAN EMBEBIDAS EN CONCRETO O EN MATERIALES RESISTENTES AL FUEGO MÍNIMO DE 15 MINUTOS.
  - EL TOMA CORRIENTE GFCI, RECIBE LA ALIMENTACION QUE VIENE DEL BREAKER, ENTRA POR LOS BORNES MARCADOS "LINE" CONECTANDO LA FASE EN "HOT" Y EL NEUTRO EN "WHITE", SIEMPRE. DE ESTE TOMA SE PUEDEN CONECTAR HASTA 6 TOMAS NORMALES DE LOS BORNES MARCADOS "LOAD", CONSERVANDO LA CONEXION DE LA FASE Y EL NEUTRO COMO SE DIJO ANTERIORMENTE Y TAMBIEN QUEDAN PROTEGIDOS (VER DETALLE) Y SE DISTINGUEN EN PLANOS CON LETRA "G" JUNTO AL NUMERO DEL CIRCUITO.

SALIDAS TOMACORRIENTES PISO 1  
ESC. S/N

DETALLE TV  
ESC. S/N

**DIODO**  
TECH LIFE

DIODO TECHNOLOGY S.A.S  
CARRERA 50FF # 8 SUR 27 OFICINA 410  
EDIFICIO EMPRESARIAL 808  
MEDELLÍN, ANTIOQUIA  
TEL: 3221340  
CEL: 3013937005  
EMAIL: CONTANCTO@DIODOTECH.COM

PROYECTO: CASA SIERRA PALMA 40  
UBICACIÓN: ENVIGADO  
PROPIETARIO:

CONTIENE: SALIDAS TOMACORRIENTES P1  
DISEÑO: JULIAN QUINTERO  
DIBUJÓ: JULIAN QUINTERO

REVISÓ: JULIAN QUINTERO  
FECHA: 17/12/2025

ACTUALIZACIONES  
N° DE PLANO  
1/6  
ESCALA  
S/N

FIRMA DE APROBACIÓN:


FECHA DE ELABORACIÓN:  
17/12/2025  
MAT: AN205-123158



CUADRO DE CARGAS TMB  
ESC. S/N




10. EL TOMA CORRIENTE GFCl, RECIBE LA ALIMENTACION QUE VIENE DEL BREAKER, ENTRA POR LOS BORNES MARCADOS "LINE" CONECTANDO LA FASE EN "HOT" Y EL NEUTRO EN "WHITE", SIEMPRE. DE ESTE TOMA SE PUEDEN CONECTAR HASTA 6 Tomas NORMALES DE LOS BORNES MARCADOS "LOAD", CONSERVANDO LA CONEXION DE LA FASE Y EL NEUTRO COMO SE DIJO ANTERIORMENTE Y TAMBIEN QUEDAN PROTEGIDOS (VER DETALLE) Y SE DISTINGUEN EN PLANOS CON LETRA "G" JUNTO AL NUMERO DEL CIRCUITO.

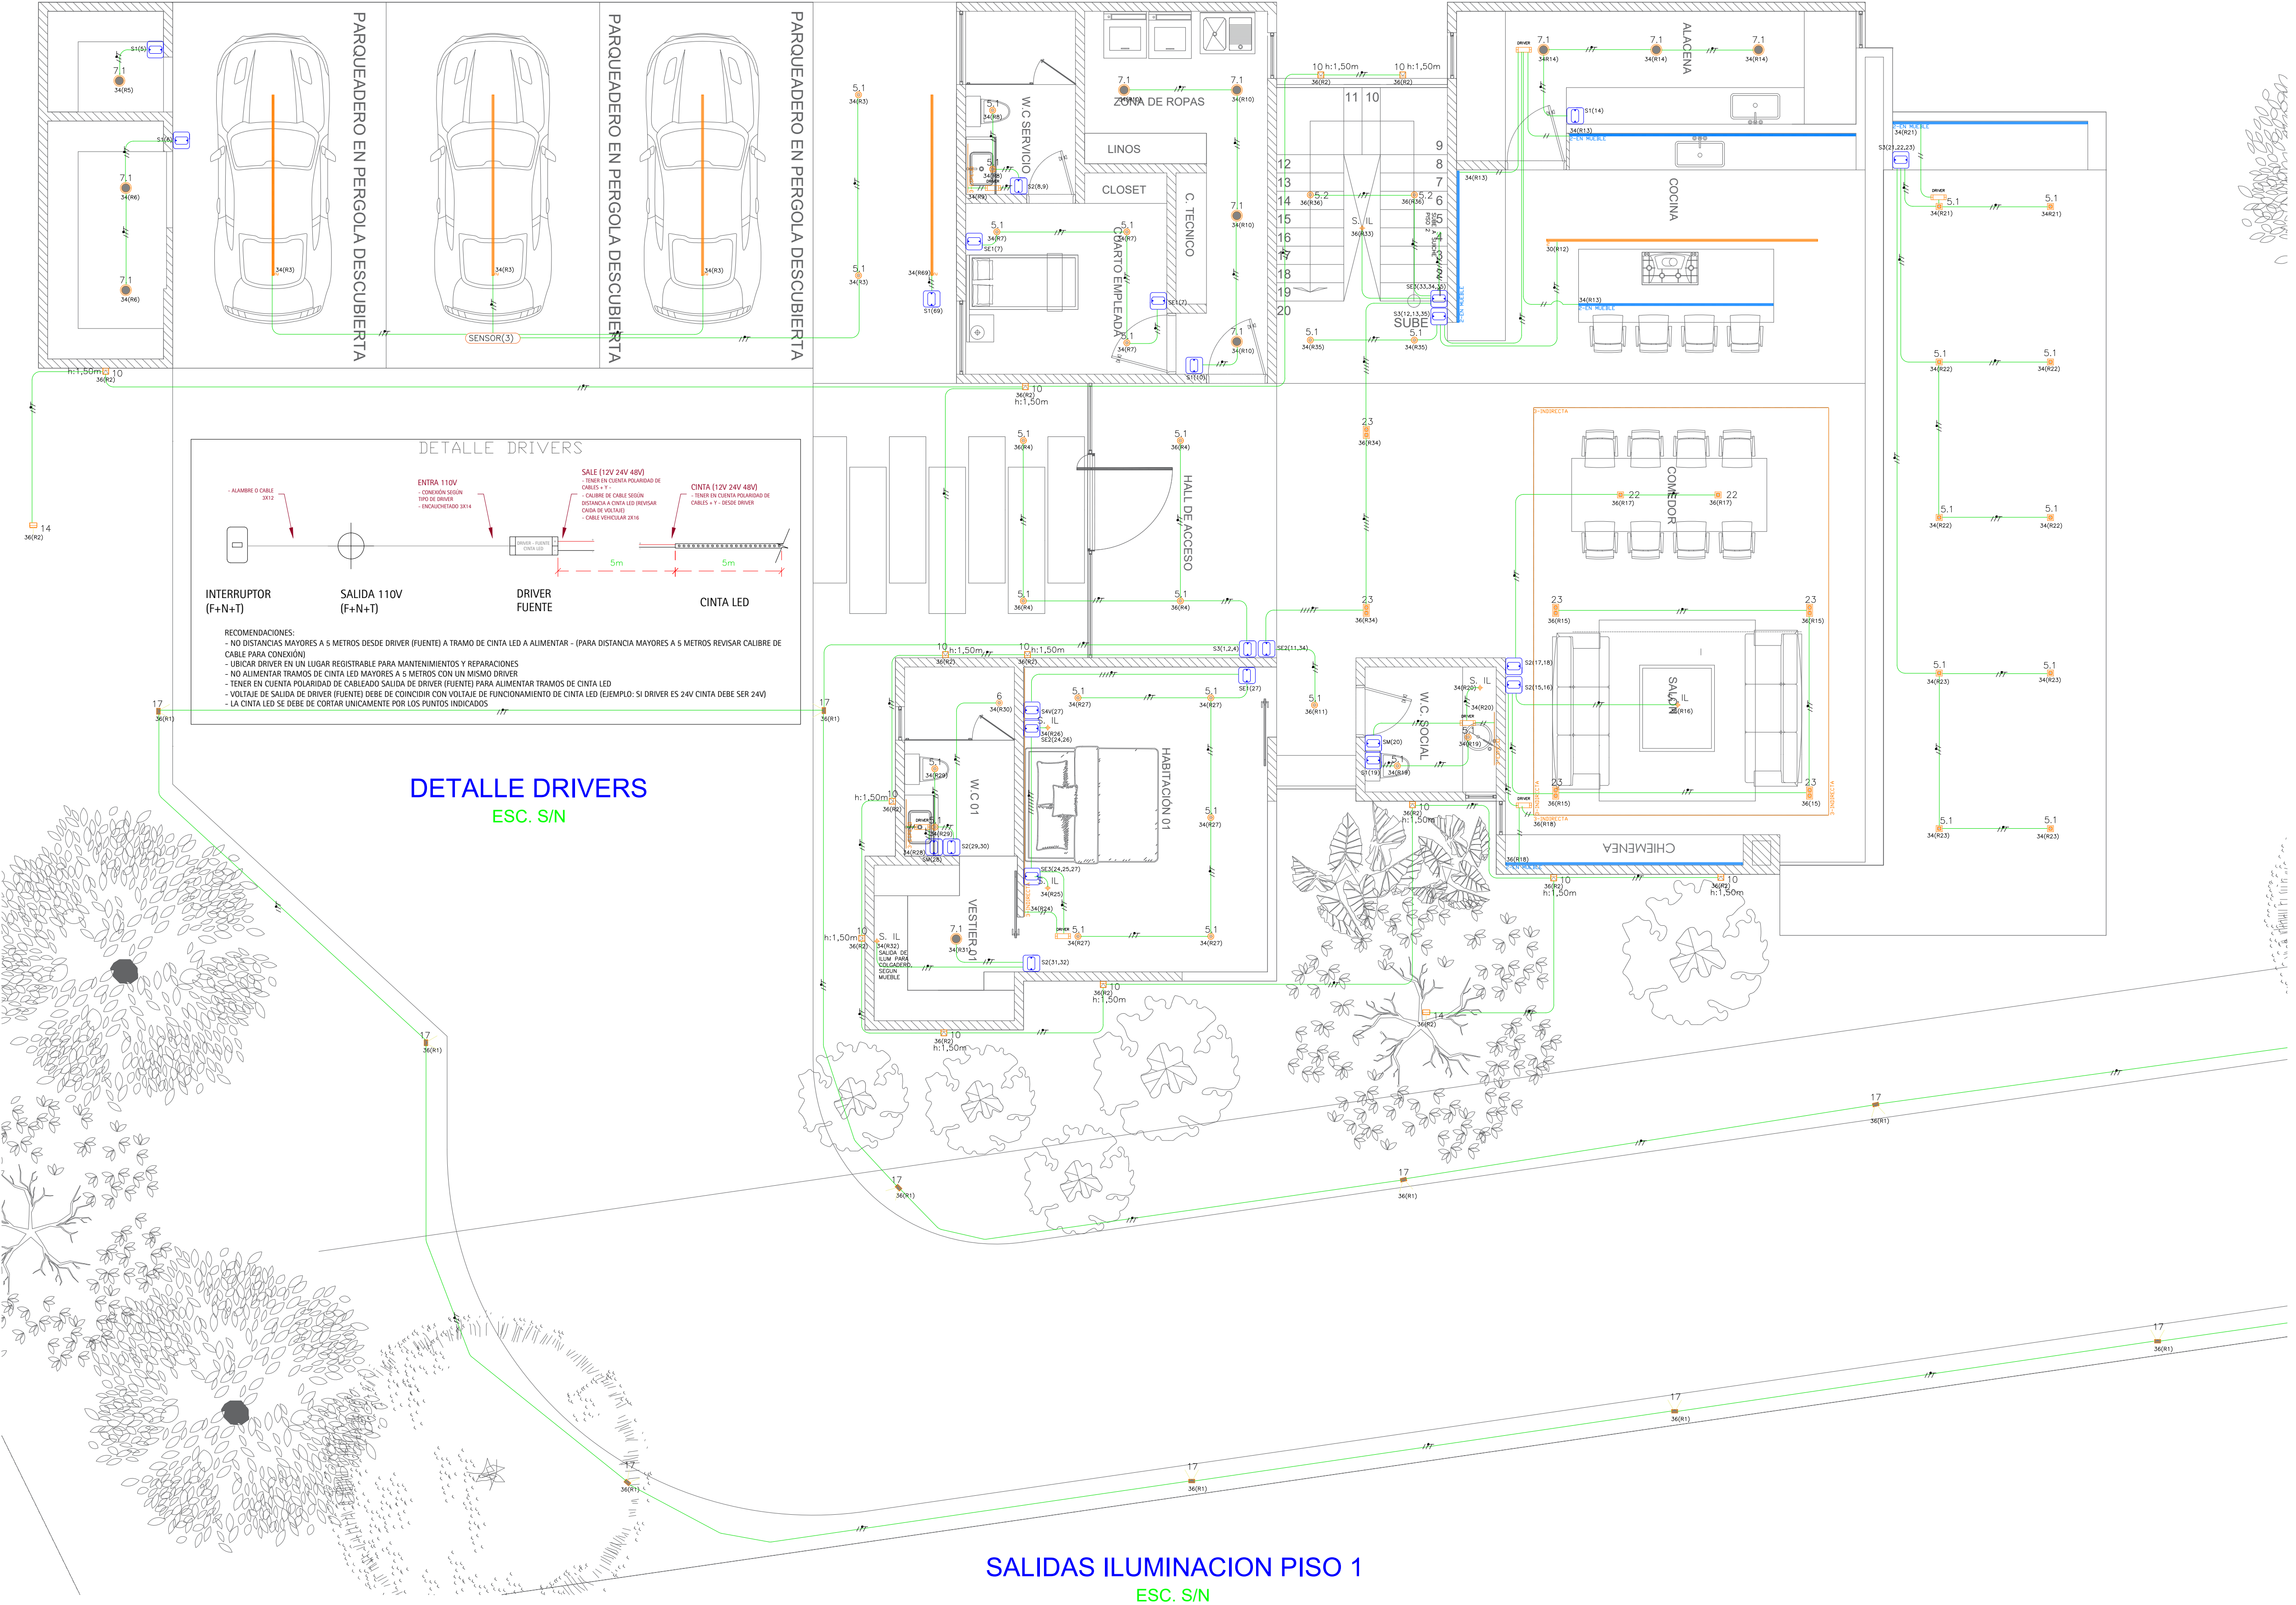

| ILUMINACIÓN |   |
|-------------|---|
|             | Luminaria tipo lineal LED para incrustar en cielo con difusor opalizado                                                                   |
|             | Iluminación tipo lineal de descolgar o sobreponer                                                                                         |
|             | Iluminación tipo perfil en aluminio con cinta LED - ubicación y tipo de perfil según detalle - driver registrable 24V                     |
|             | Iluminación tipo cinta LED sobre platina en aluminio para iluminación indirecta - ubicación y tipo según detalle - driver registrable 24V |
|             | Iluminación tipo cinta LED sobre platina en aluminio para iluminación indirecta - ubicación y tipo según detalle - driver registrable 24V |
|             | Sistema riel en aluminio para incrustar o sobreponer en cielo falso tipo magnetico                                                        |
|             | Bala LED para incrustar en piso tipo floorlight para instalar en piso                                                                     |
|             | Downlight escualzable recesada para bombillo LED GU10 para incrustar en cielo falso                                                       |
|             | Downlight recesada con LED integrado para incrustar en cielo falso                                                                        |
|             | Downlight para bombillo LED GU10 para incrustar en cielo falso IP65                                                                       |
|             | Downlight LED con difusor opalizado para incrustar en cielo                                                                               |
|             | Downlight LED con difusor opalizado para incrustar en cielo                                                                               |
|             | Spot LED direccionable escualzable con plafón para sobreponer en cielo                                                                    |
|             | Downlight mini con LED integrado para incrustar en cielo falso recesada                                                                   |
|             | Aplicle de sobreponer en pared efecto directo / indirecto                                                                                 |
|             | Luminaria tipo spot direccionable para instalación en riel magnetico                                                                      |
|             | Spot LED para jardines para exterior con herraje para fijación en jardines                                                                |
|             | Proyector LED para jardines para exterior con herraje para fijación en jardines                                                           |
|             | Cilindro de sobreponer LED para sobreponer en estructura para exteriores                                                                  |
|             | Cardan grande sencilla de incrustar para bombillo DAR15 LED                                                                               |
|             | Bolardo para sobreponer en piso LED para exterior                                                                                         |
|             | Salida para iluminación decorativa o luminaria especial                                                                                   |
|             | Driver para alimentación de cinta LED - se recomienda en ubicación registrable                                                            |
|             | Cardan grande doble de incrustar para bombillo DAR15 LED                                                                                  |
|             | Cardan pequeña doble de incrustar para bombillo GU10 LED                                                                                  |

| CAJAS SUICHERIA   |   |
|---|---|
| Todos los suiches, incluyendo conmutables, deben tener fase, neutro, regreso y tierra; todos con puntas fuera de la caja. Cajas con 3 cm de profundidad del revoque. Ventaja de puntas de cables 30cm. |   |
|   | S1: Suiche sencillo: Caja 2x4 de PVC vertical, o 4x4 con tapa flush. Posición, ver detalle.                      |
|   | S2: Suiche doble: Caja 4x4 de PVC sin tapa flush. Posición, ver detalle.                                         |
|   | S3: Suiche triple: Caja 4x6 de PVC horizontal. Caja suministrada por Diodo Technology. Posición, ver detalle.    |
|   | S4: Suiche cuadruple: Caja 4x8 de PVC horizontal. Caja suministrada por Diodo Technology. Posición, ver detalle. |

| NOTAS   |                                                     |
|---|-----------------------------------------------------|
| En los suiches hay presentes unas letras el cual significan lo siguiente:<br>1. S1= Suiche sencillo<br>2. S2= Suiche doble<br>3. S3= Suiche triple<br>4. SE1= Suiche en escala sencillo<br>5. SE2= Suiche en escala doble<br>6. SE3= suiche en escala triple<br>7. S4V= Suiche sencillo 4 vias<br>8. D= Dimmer<br>9. A= Auxiliar<br>10. B= Botonera<br>11. S= Sensor de movimiento |                                                     |
|   | Ejm: S2(A,B)<br>Suiche doble<br>Nombre regreso      |
| En cada luminaria esta el nombre del regreso el cual pertenece a un suiche.   |                                                     |
|   | Ejm: #AB<br>Luminaria<br>#circuit<br>Nombre regreso |

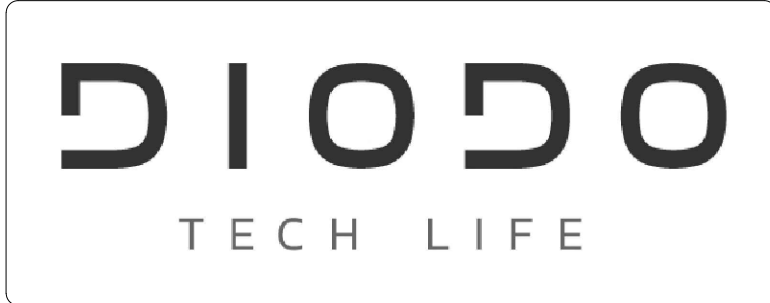

DIDO TECHNOLOGY S.A.S  
CARRERA 50FF # 8 SUR 27 OFICINA 410  
EDIFICIO EMPRESARIAL 808  
MEDELLÍN, ANTIOQUIA  
TEL: 3221340  
CEL: 3013937005  
EMAIL: CONTANCTO@DIDODOTECH.COM

PROYECTO: CASA SIERRA PALMA 40  
UBICACIÓN: ENVIGADO  
PROPIETARIO:

CONTIENE: SALIDAS ILUMINACION P1  
DISEÑO: JULIAN QUINTERO  
DIBUJÓ: JULIAN QUINTERO


REVISÓ: JULIAN QUINTERO  
FECHA: 17/12/2025

ACTUALIZACIONES  
N° DE PLANO  
3/6  
ESCALA  
S/N

FIRMA DE APROBACIÓN:  
FECHA DE ELABORACIÓN: 17/12/2025  
MAT: AN205-123158




| <h2 style="text-align: center;">NOTAS</h2>   |                                                                                       |                   |
|---|---------------------------------------------------------------------------------------|-------------------|
| <p>En los suiches hay presentes unas letras el cual significan lo siguiente:</p> <ol style="list-style-type: none"> <li>1. S1= Suiche sencillo</li> <li>2. S2= Suiche doble</li> <li>3. S3= Suiche triple</li> <li>4. SE1= Suiche en escala sencillo</li> <li>5. SE2= Suiche en escala doble</li> <li>6. SE3= suiche en escala triple</li> <li>7. S4V= Suiche sencillo 4 vias</li> <li>8. D= Dimmer</li> <li>9. A= Auxiliiar</li> <li>10. B= Botonera</li> <li>11. S= Sensor de movimiento</li> </ol> |                                                                                       |                   |
| <p>Ejm:<br/>S2(A,B)</p>   |                                                                                       |                   |
| Suiche doble   |  | Nombre<br>regreso |
| <p>En cada luminaria esta el nombre del regreso el cual pertenece a un suiche.</p>   |                                                                                       |                   |
| <p>Ejm:</p>   |                                                                                       |                   |
| Luminaria   |  | #AB               |
| #circuito<br>electrico   |                                                                                       | Nombre<br>regreso |

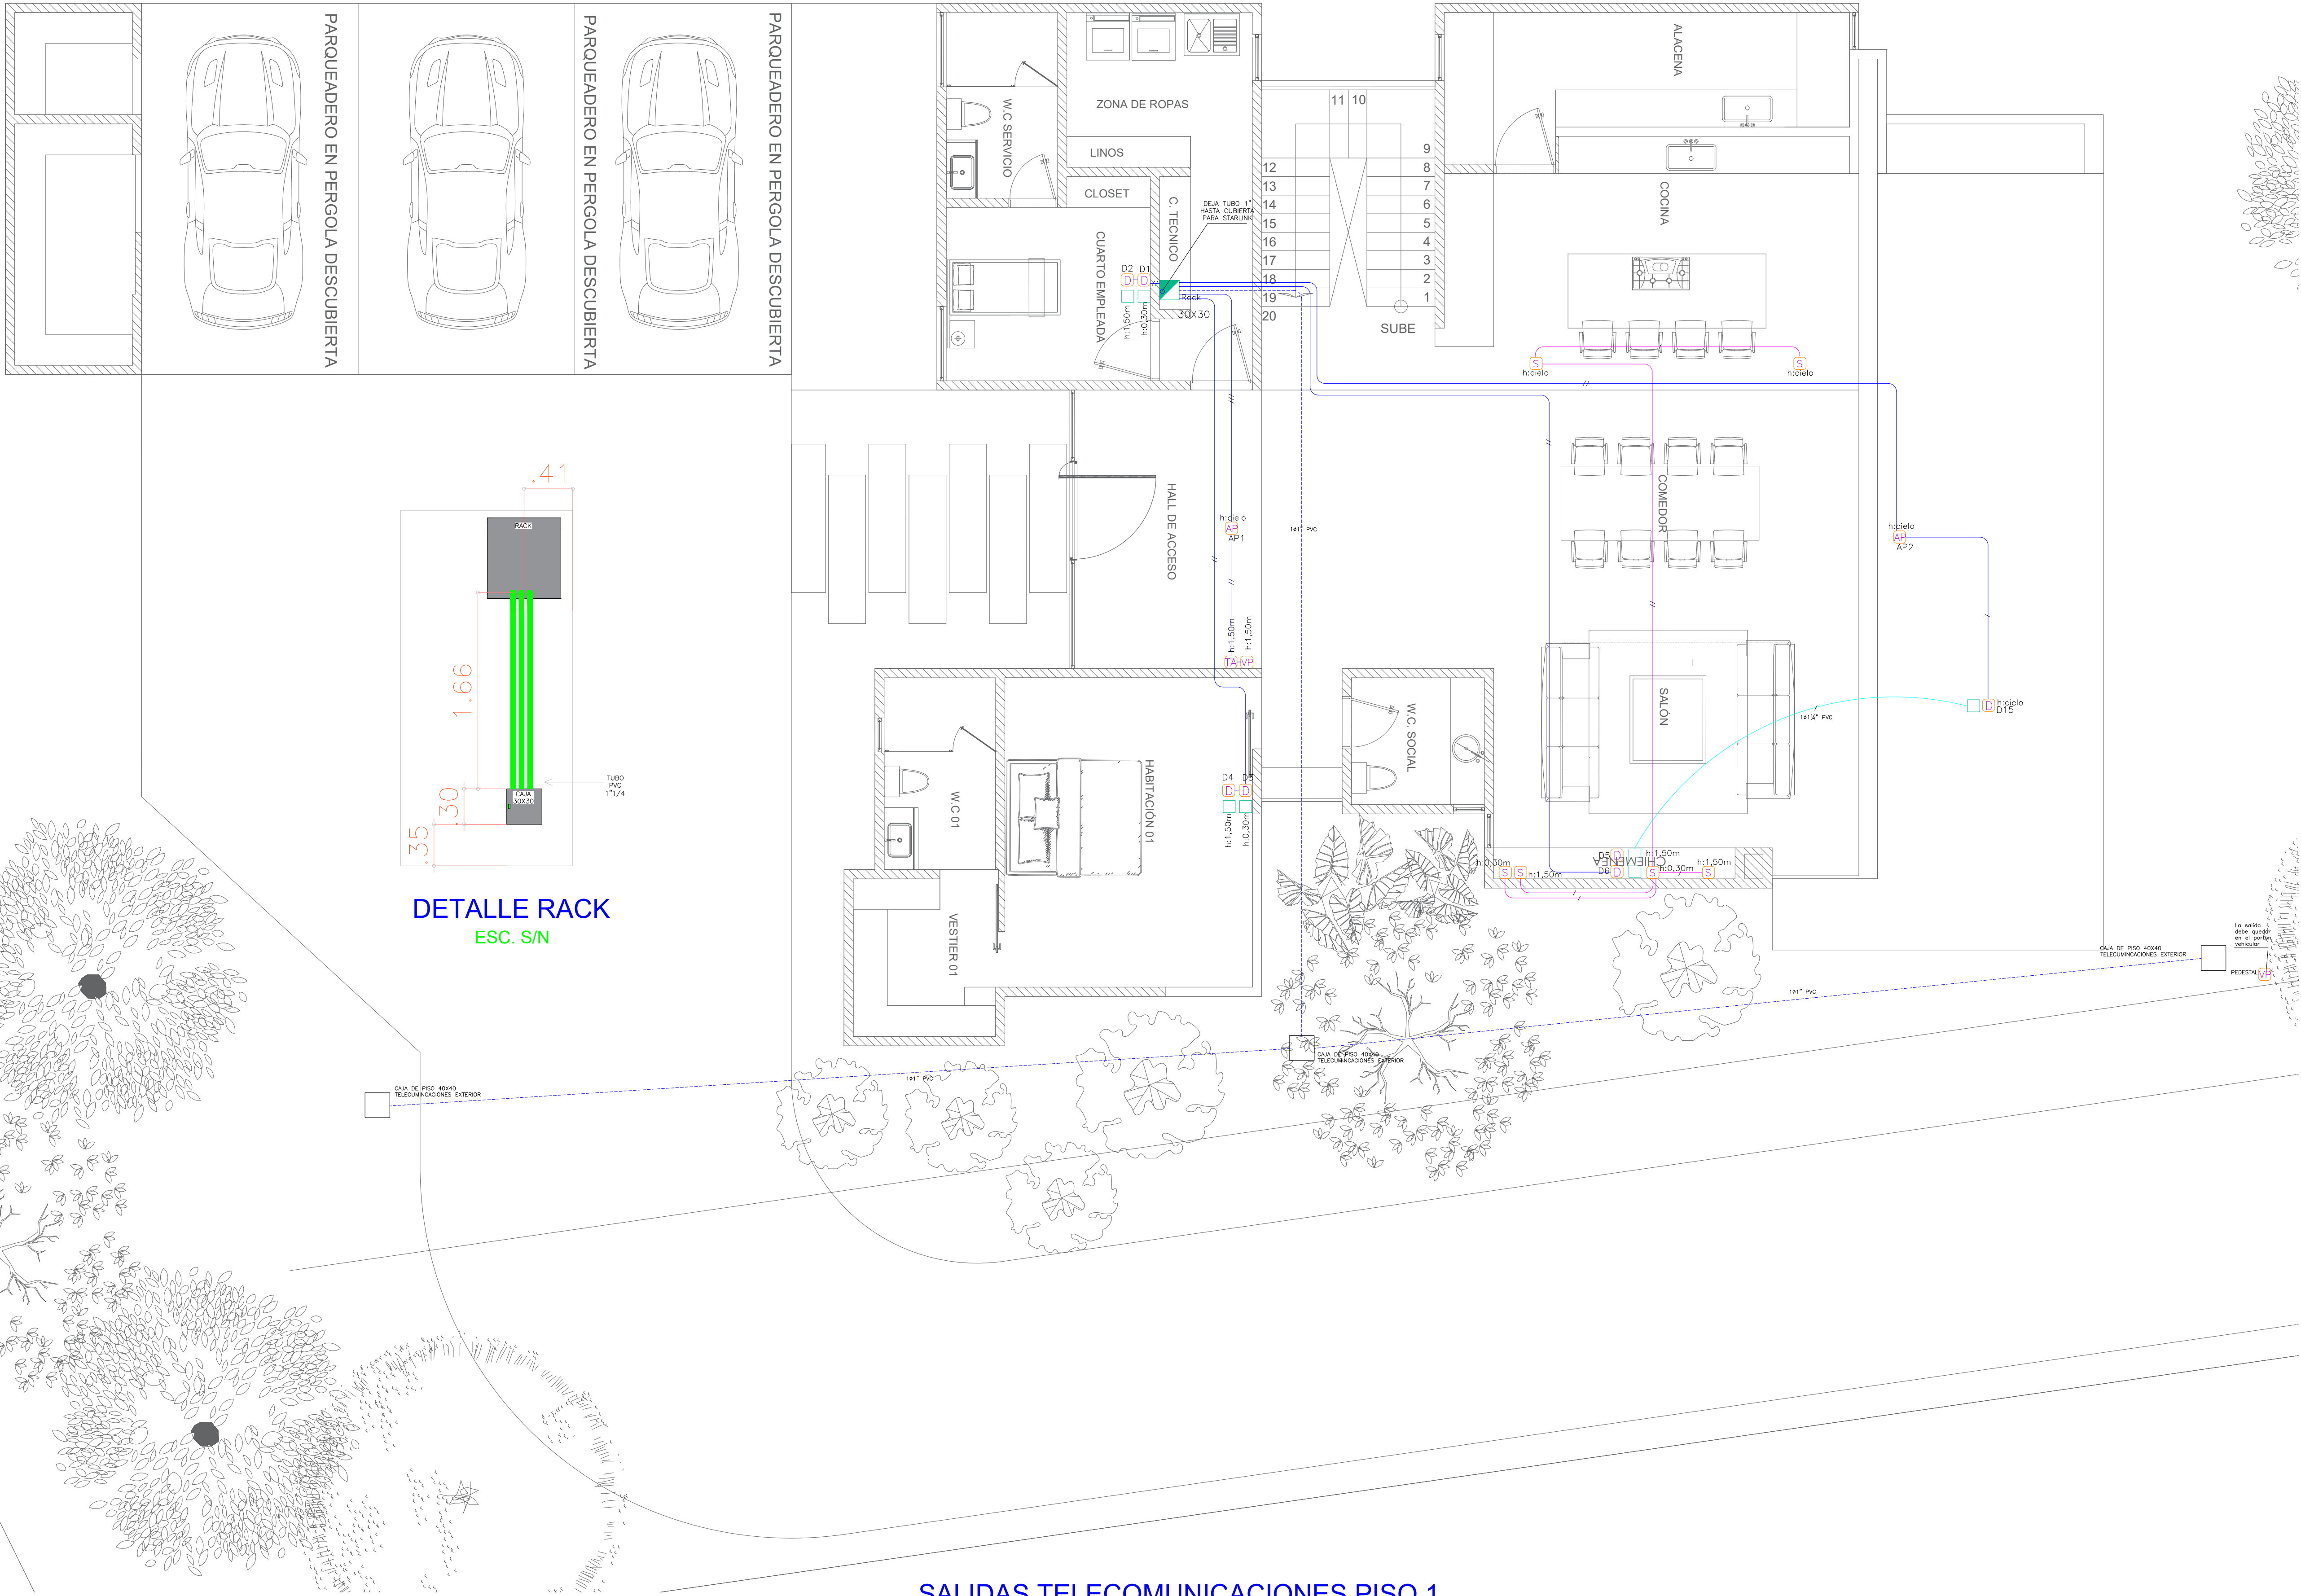

| CONVENCIONES TELECOMUNICACIONES |  |                              |
|---------------------------------|--|------------------------------|
| 1                               |  | PASACABLES                   |
| 2                               |  | TABLERO DE DISTRIBUCION      |
| 3                               |  | TOMA DE TELEVISIÓN           |
| 4                               |  | CAJA 30X30x10cm FONDO MADERA |
| 5                               |  | TOMA DE DATOS                |
| 6                               |  | VIDEO PORTERO                |
| 7                               |  | TECLADO DE ALARMA            |
| 8                               |  | ACCESS POINT                 |
| 9                               |  | TUBERÍA DATOS CIELO O PARED  |
| 10                              |  | TUBERÍA DATOS POR PISO       |
| 11                              |  | TUBERIA DE SONIDO            |
| 12                              |  | TUBERIA 1 ¼ PARA HDMI        |

- NOTAS:
- TUBERIA Y ALAMBRE NO ESPECIFICADOS SON  $\varnothing 3/4"$  PVC No.12 AWG, THHN.
  - TUBERIA Y ALAMBRE NO ESPECIFICADOS EN CIELOS FALSOS PARA REDES SOBREPUESTAS SON  $\varnothing 3/4"$  INTERFLEX TIPO HFR Ó SCHEDULE 40 Y No.12 AWG, LSZH O LIBRE DE HALÓGENOS.
  - LAS CAJAS DONDE LLEGUE UN TUBO DE  $\varnothing 3/4"$  Ó MAS SERÁN 4x4 INTERFLEX CON TAPA FLUSH.
  - LAS CAJAS PARA LAS SALIDAS DE, TELEVISION Y TELEFONO SERÁN 4x4 INTERFLEX CON TAPA FLUSH.
  - CODIGO DE COLORES: NEUTRO=BLANCO, TIERRA=VERDE. ESTOS COLORES NO PODRÁN SER UTILIZADOS PARA NINGUN OTRO CONDUCTOR.FASES: ROJO O NEGRO, DE ACUERDO A LO ESTIPULADO EN EL RETIE PARA TALEROS MONOFÁSICOS Y TRAFIO EN CONEXIÓN DELTA-ESTRELLA ATERRIZADO.
  - LA LINEA DE POLO A TIERRA IRA A LO LARGO DE TODA LA INSTALACION ELECTRICA EN CONDUCTOR COBRE, TW No.12 VERDE.
  - TODA SALIDA ELECTRICA DEBE QUEDAR A POR LO MENOS 30 cms DE LAS VALVULAS Ó SALIDAS DE GAS.
  - ALTURAS NO ESPECIFICADAS PARA SALIDAS SERA DE 30CM NIVEL PISO ACABADO.
  - LOS TUBOS POR CIELOS DEBERÁN SER EMT Ó SCH40 DE ACUERDO AL LITERAL 20.6.1.2 REQUISITOS DE INSTALACIÓN LITERAL H. NO SE DEBEN INSTALAR TUBERIAS NO METÁLICAS LIVIANAS (TIPO A), EXPUESTAS NI EN CIELOS FALSOS; SOLO SE ADMITEN SI VAN EMBEBIDAS EN CONCRETO O EN MATERIALES RESISTENTES AL FUEGO MÍNIMO DE 15 MINUTOS.
  - EL TOMA CORRIENTE GFCI, RECIBE LA ALIMENTACION QUE VIENE DEL BREAKER, ENTRA POR LOS BORNES MARCADOS "LINE" CONECTANDO LA FASE EN "HOT" Y EL NEUTRO EN "WHITE", SIEMPRE. DE ESTE TOMA SE PUEDEN CONECTAR HASTA 6 TOMAS NORMALES DE LOS BORNES MARCADOS "LOAD", CONSERVANDO LA CONEXION DE LA FASE Y EL NEUTRO COMO SE DIJO ANTERIORMENTE Y TAMBIEN QUEDAN PROTEGIDOS (VER DETALLE) Y SE DISTINGUEN EN PLANOS CON LETRA "G" JUNTO AL NUMERO DEL CIRCUITO.

SALIDAS TELECOMUNICACIONES PISO 1  
ESC. S/N

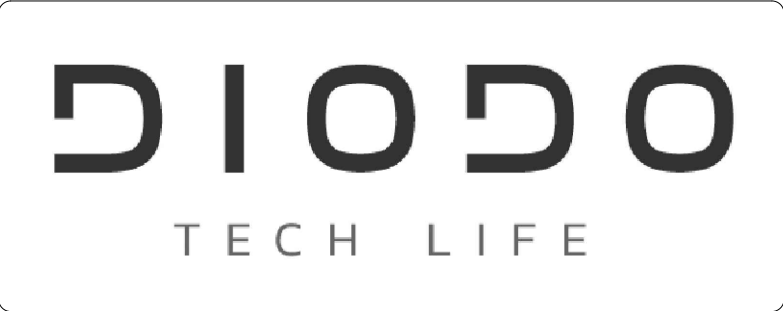

DIODO TECHNOLOGY S.A.S  
CARRERA 50FF # 8 SUR 27 OFICINA 410  
EDIFICIO EMPRESARIAL 808  
MEDELLÍN, ANTIOQUIA  
TEL: 3221340  
CEL: 3013937005  
EMAIL: CONTANCTO@DIODOTECH.COM


PROYECTO: CASA SIERRA PALMA 40  
UBICACIÓN: ENVIGADO  
PROPIETARIO:

CONTIENE: SALIDAS TELECOMUNIC P1  
DISEÑO: JULIAN QUINTERO  
DIBUJÓ: JULIAN QUINTERO


REVISÓ: JULIAN QUINTERO  
FECHA: 17/12/2025

| ACTUALIZACIONES | N° DE PLANO |
|-----------------|-------------|
| V1              | 5/6         |
|                 | ESCALA      |
|                 | S/N         |

FIRMA DE APROBACIÓN:  
FECHA DE ELABORACIÓN:  
17/12/2025 MAT: AN205-123158

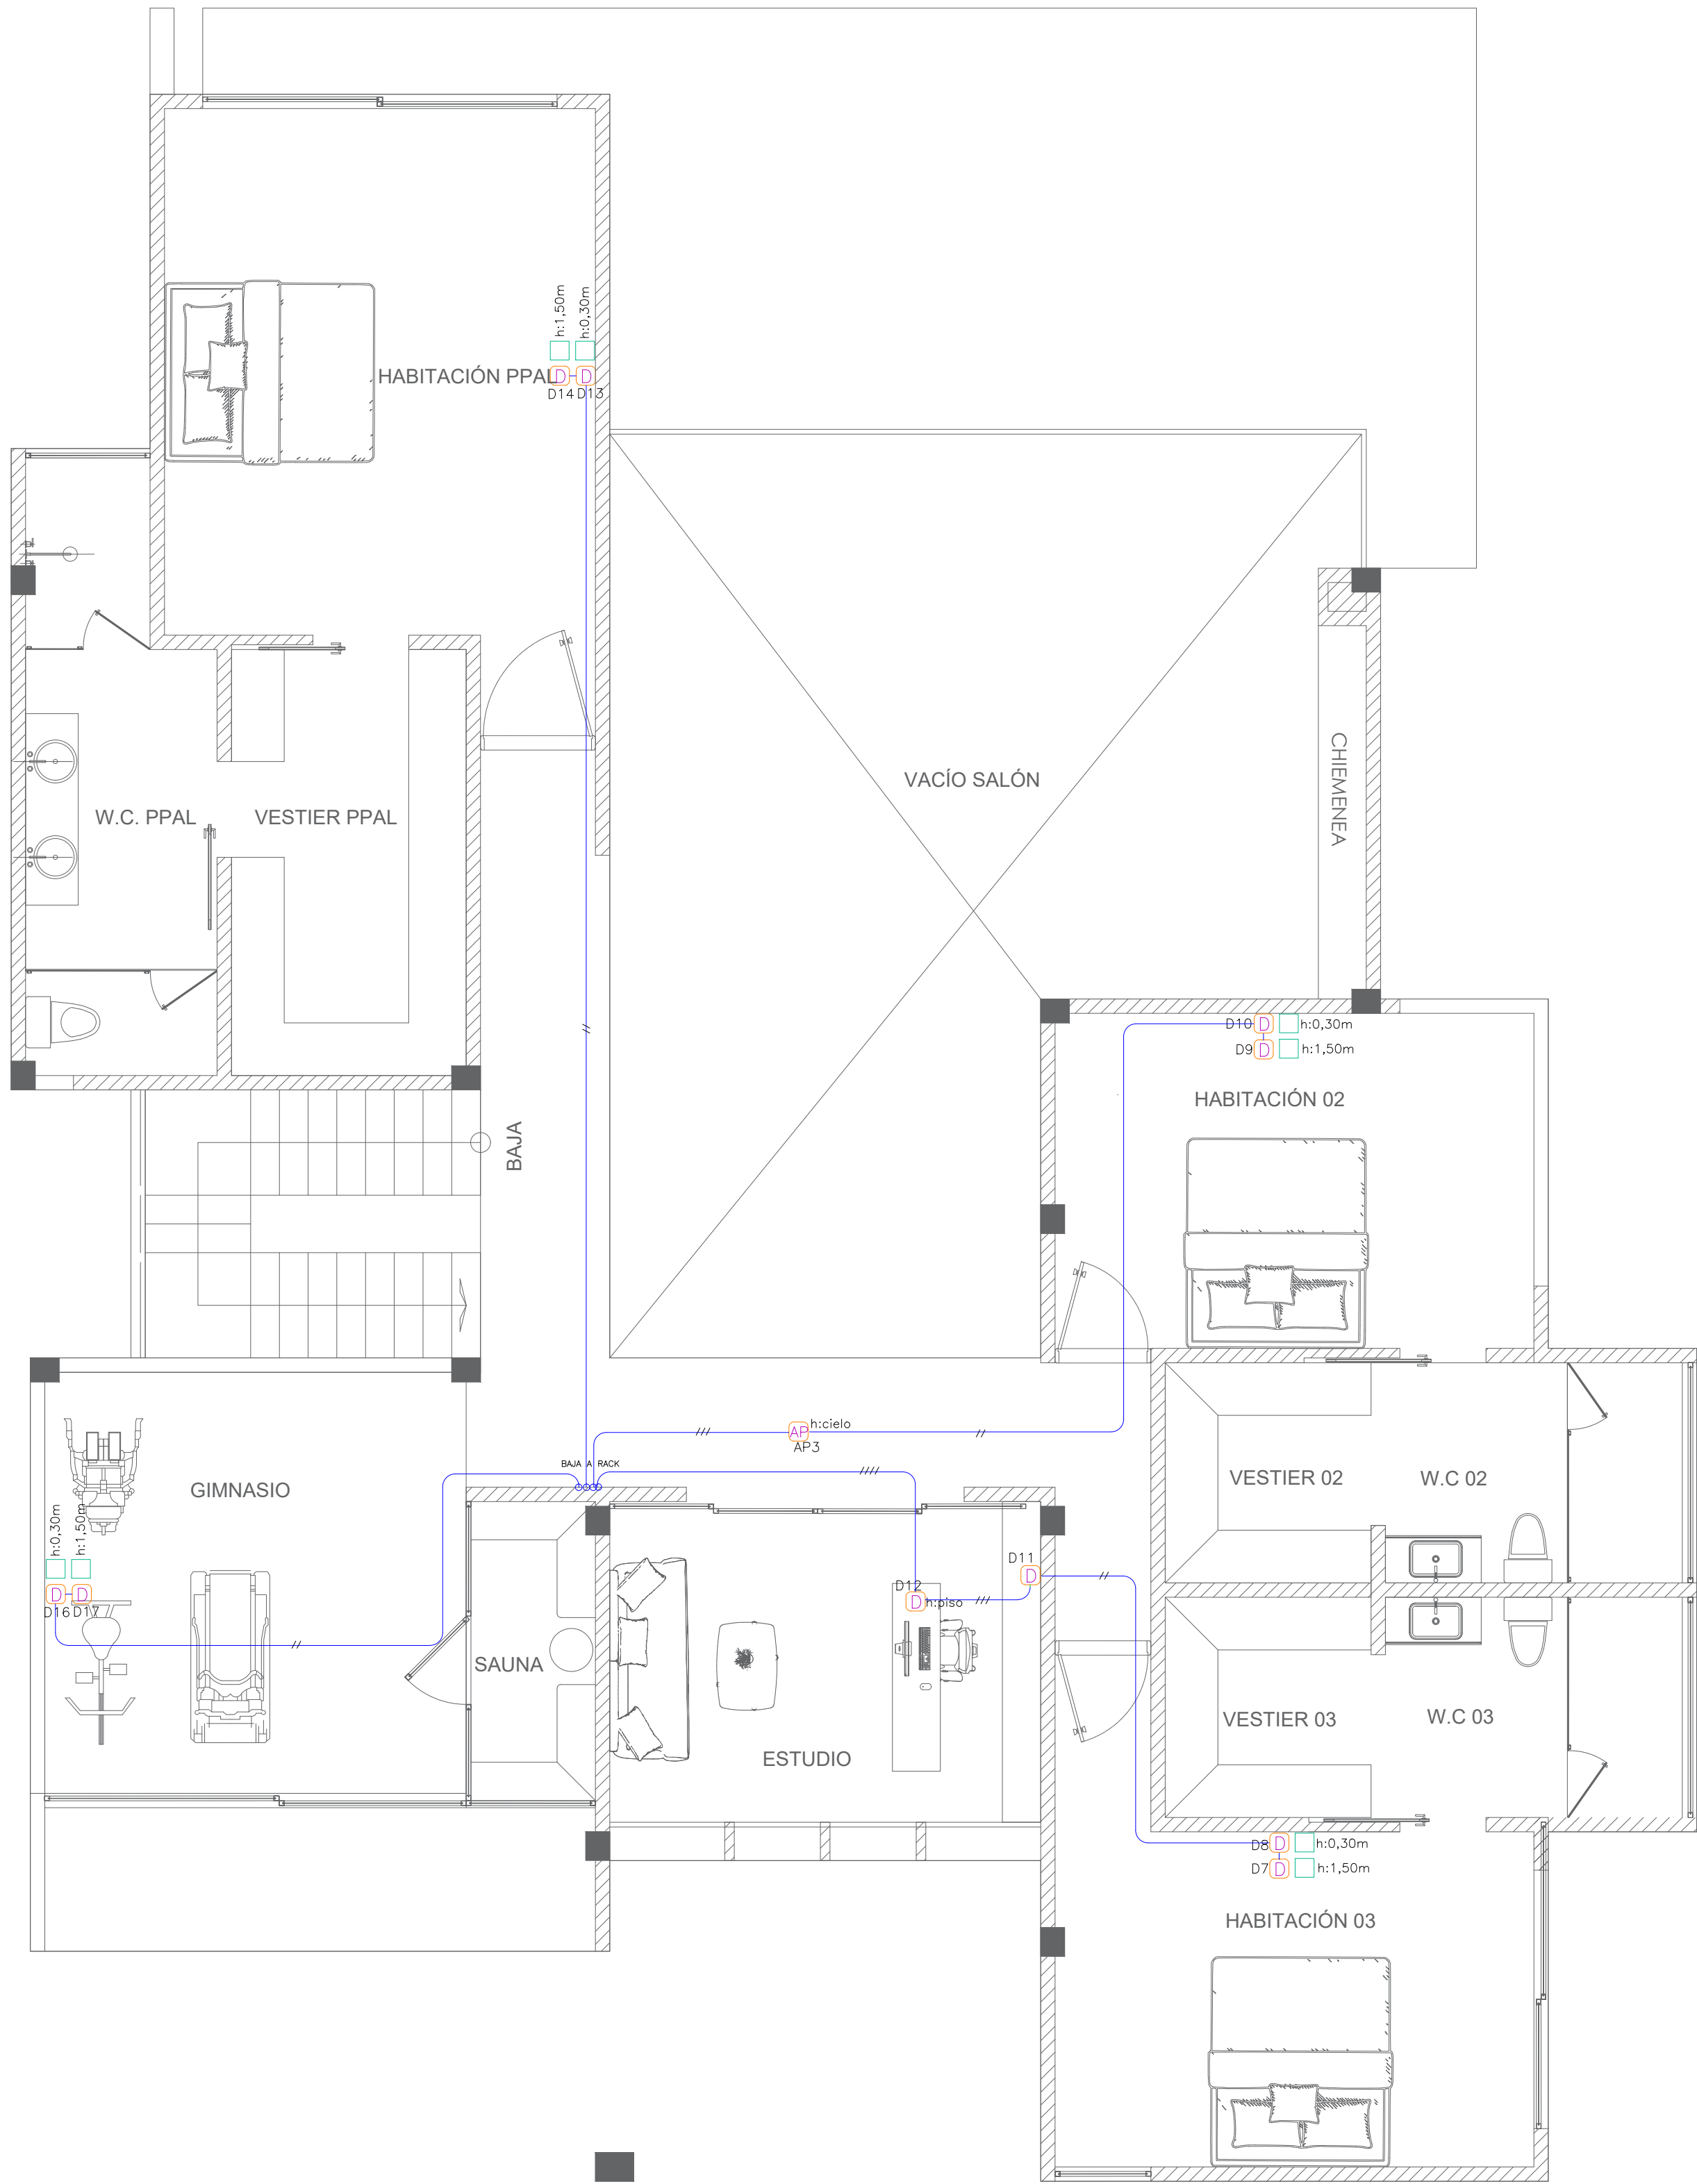


SALIDAS TELECOMUNICACIONES PISO 2  
ESC. S/N

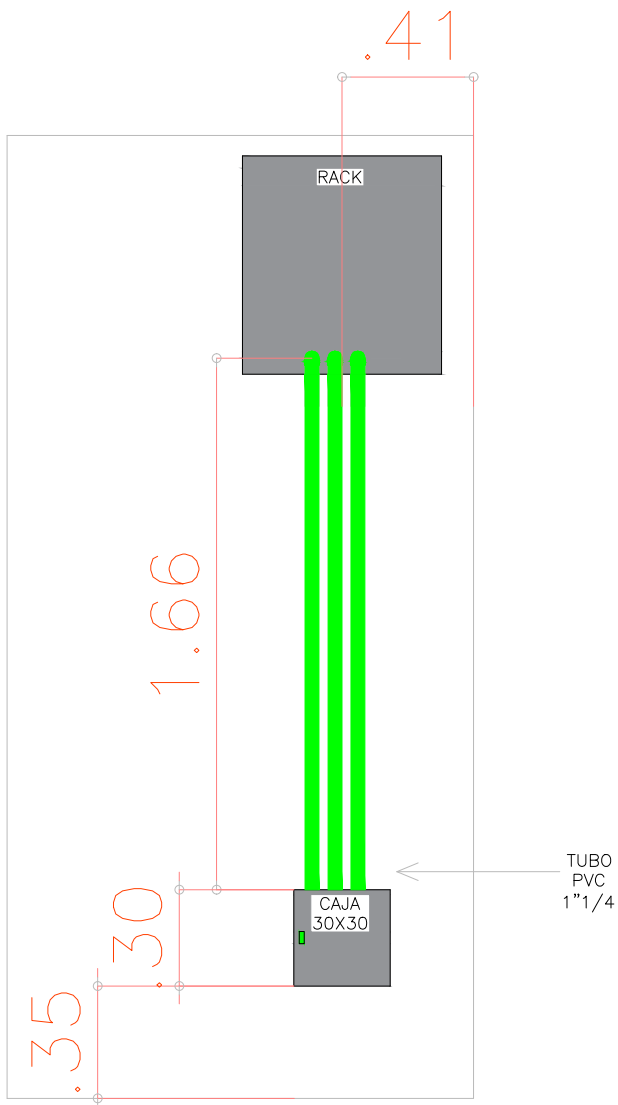

DETALLE RACK  
ESC. S/N

| CONVENCIONES TELECOMUNICACIONES |  |                              |
|---------------------------------|--|------------------------------|
| 1                               |  | PASACABLES                   |
| 2                               |  | TABLERO DE DISTRIBUCION      |
| 3                               |  | TOMA DE TELEVISIÓN           |
| 4                               |  | CAJA 30X30x10cm FONDO MADERA |
| 5                               |  | TOMA DE DATOS                |
| 6                               |  | VIDEO PORTERO                |
| 7                               |  | TECLADO DE ALARMA            |
| 8                               |  | ACCESS POINT                 |
| 9                               |  | TUBERÍA DATOS CIELO O PARED  |
| 10                              |  | TUBERÍA DATOS POR PISO       |
| 11                              |  | TUBERIA DE SONIDO            |
| 12                              |  | TUBERIA 1 1/4 PARA HDMI      |

- NOTAS:
- TUBERIA Y ALAMBRE NO ESPECIFICADOS SON  $\varnothing 3/4"$  PVC No.12 AWG, THHN.
  - TUBERIA Y ALAMBRE NO ESPECIFICADOS EN CIELOS FALSOS PARA REDES SOBREPUESTAS SON  $\varnothing 3/4"$  INTERFLEX TIPO HFR Ó SCHEDULE 40 Y No.12 AWG, LSZH O LIBRE DE HALÓGENOS.
  - LAS CAJAS DONDE LLEGUE UN TUBO DE  $\varnothing 3/4"$  Ó MAS SERÁN 4x4 INTERFLEX CON TAPA FLUSH.
  - LAS CAJAS PARA LAS SALIDAS DE, TELEVISION Y TELEFONO SERÁN 4x4 INTERFLEX CON TAPA FLUSH.
  - CODIGO DE COLORES: NEUTRO=BLANCO, TIERRA=VERDE. ESTOS COLORES NO PODRÁN SER UTILIZADOS PARA NINGUN OTRO CONDUCTOR.FASES: ROJO O NEGRO, DE ACUERDO A LO ESTIPULADO EN EL RETIE PARA TALEROS MONOFÁSICOS Y TRAFIO EN CONEXIÓN DELTA-ESTRELLA ATERRIZADO.
  - LA LINEA DE POLO A TIERRA IRA A LO LARGO DE TODA LA INSTALACION ELECTRICA EN CONDUCTOR COBRE, TW No.12 VERDE.
  - TODA SALIDA ELECTRICA DEBE QUEDAR A POR LO MENOS 30 cms DE LAS VALVULAS Ó SALIDAS DE GAS.
  - ALTURAS NO ESPECIFICADAS PARA SALIDAS SERA DE 30CM NIVEL PISO ACABADO.
  - LOS TUBOS POR CIELOS DEBERÁN SER EMT Ó SCH40 DE ACUERDO AL LITERAL 20.6.1.2 REQUISITOS DE INSTALACIÓN LITERAL H. NO SE DEBEN INSTALAR TUBERÍAS NO METÁLICAS LIVIANAS (TIPO A), EXPUESTAS NI EN CIELOS FALSOS; SOLO SE ADMITEN SI VAN EMBEBIDAS EN CONCRETO O EN MATERIALES RESISTENTES AL FUEGO MÍNIMO DE 15 MINUTOS.
  - EL TOMA CORRIENTE GFCI, RECIBE LA ALIMENTACION QUE VIENE DEL BREAKER, ENTRA POR LOS BORNES MARCADOS "LINE" CONECTANDO LA FASE EN "HOT" Y EL NEUTRO EN "WHITE", SIEMPRE. DE ESTE TOMA SE PUEDEN CONECTAR HASTA 6 TOMAS NORMALES DE LOS BORNES MARCADOS "LOAD", CONSERVANDO LA CONEXION DE LA FASE Y EL NEUTRO COMO SE DIJO ANTERIORMENTE Y TAMBIEN QUEDAN PROTEGIDOS (VER DETALLE) Y SE DISTINGUEN EN PLANOS CON LETRA "G" JUNTO AL NUMERO DEL CIRCUITO.

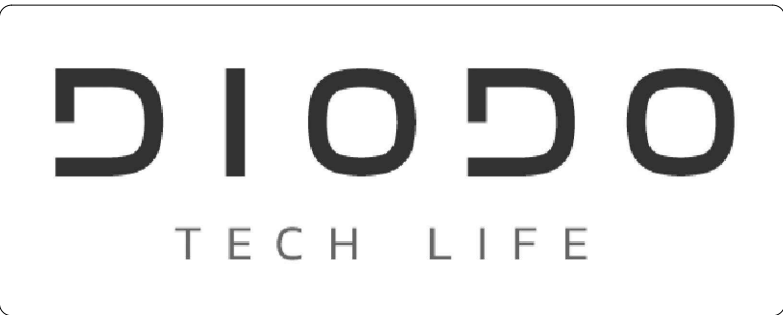

DIODO TECHNOLOGY S.A.S  
CARRERA 50FF # 8 SUR 27 OFICINA 410  
EDIFICIO EMPRESARIAL 808  
MEDELLÍN, ANTIOQUIA  
TEL: 3221340  
CEL: 3013937005  
EMAIL: CONTANCTO@DIODOTECH.COM

PROYECTO: CASA SIERRA PALMA 40  
UBICACIÓN: ENVIGADO  
PROPIETARIO:

CONTIENE: SALIDAS TELECOMUNIC P2  
DISEÑO: JULIAN QUINTERO  
DIBUJÓ: JULIAN QUINTERO

REVISO: JULIAN QUINTERO  
FECHA: 17/12/2025

| ACTUALIZACIONES | N° DE PLANO |
|-----------------|-------------|
| V1              | 6/6         |
|                 | ESCALA      |
|                 | S/N         |

FIRMA DE APROBACIÓN:  
  
FECHA DE ELABORACIÓN: 17/12/2025  
MAT: AN205-123158